
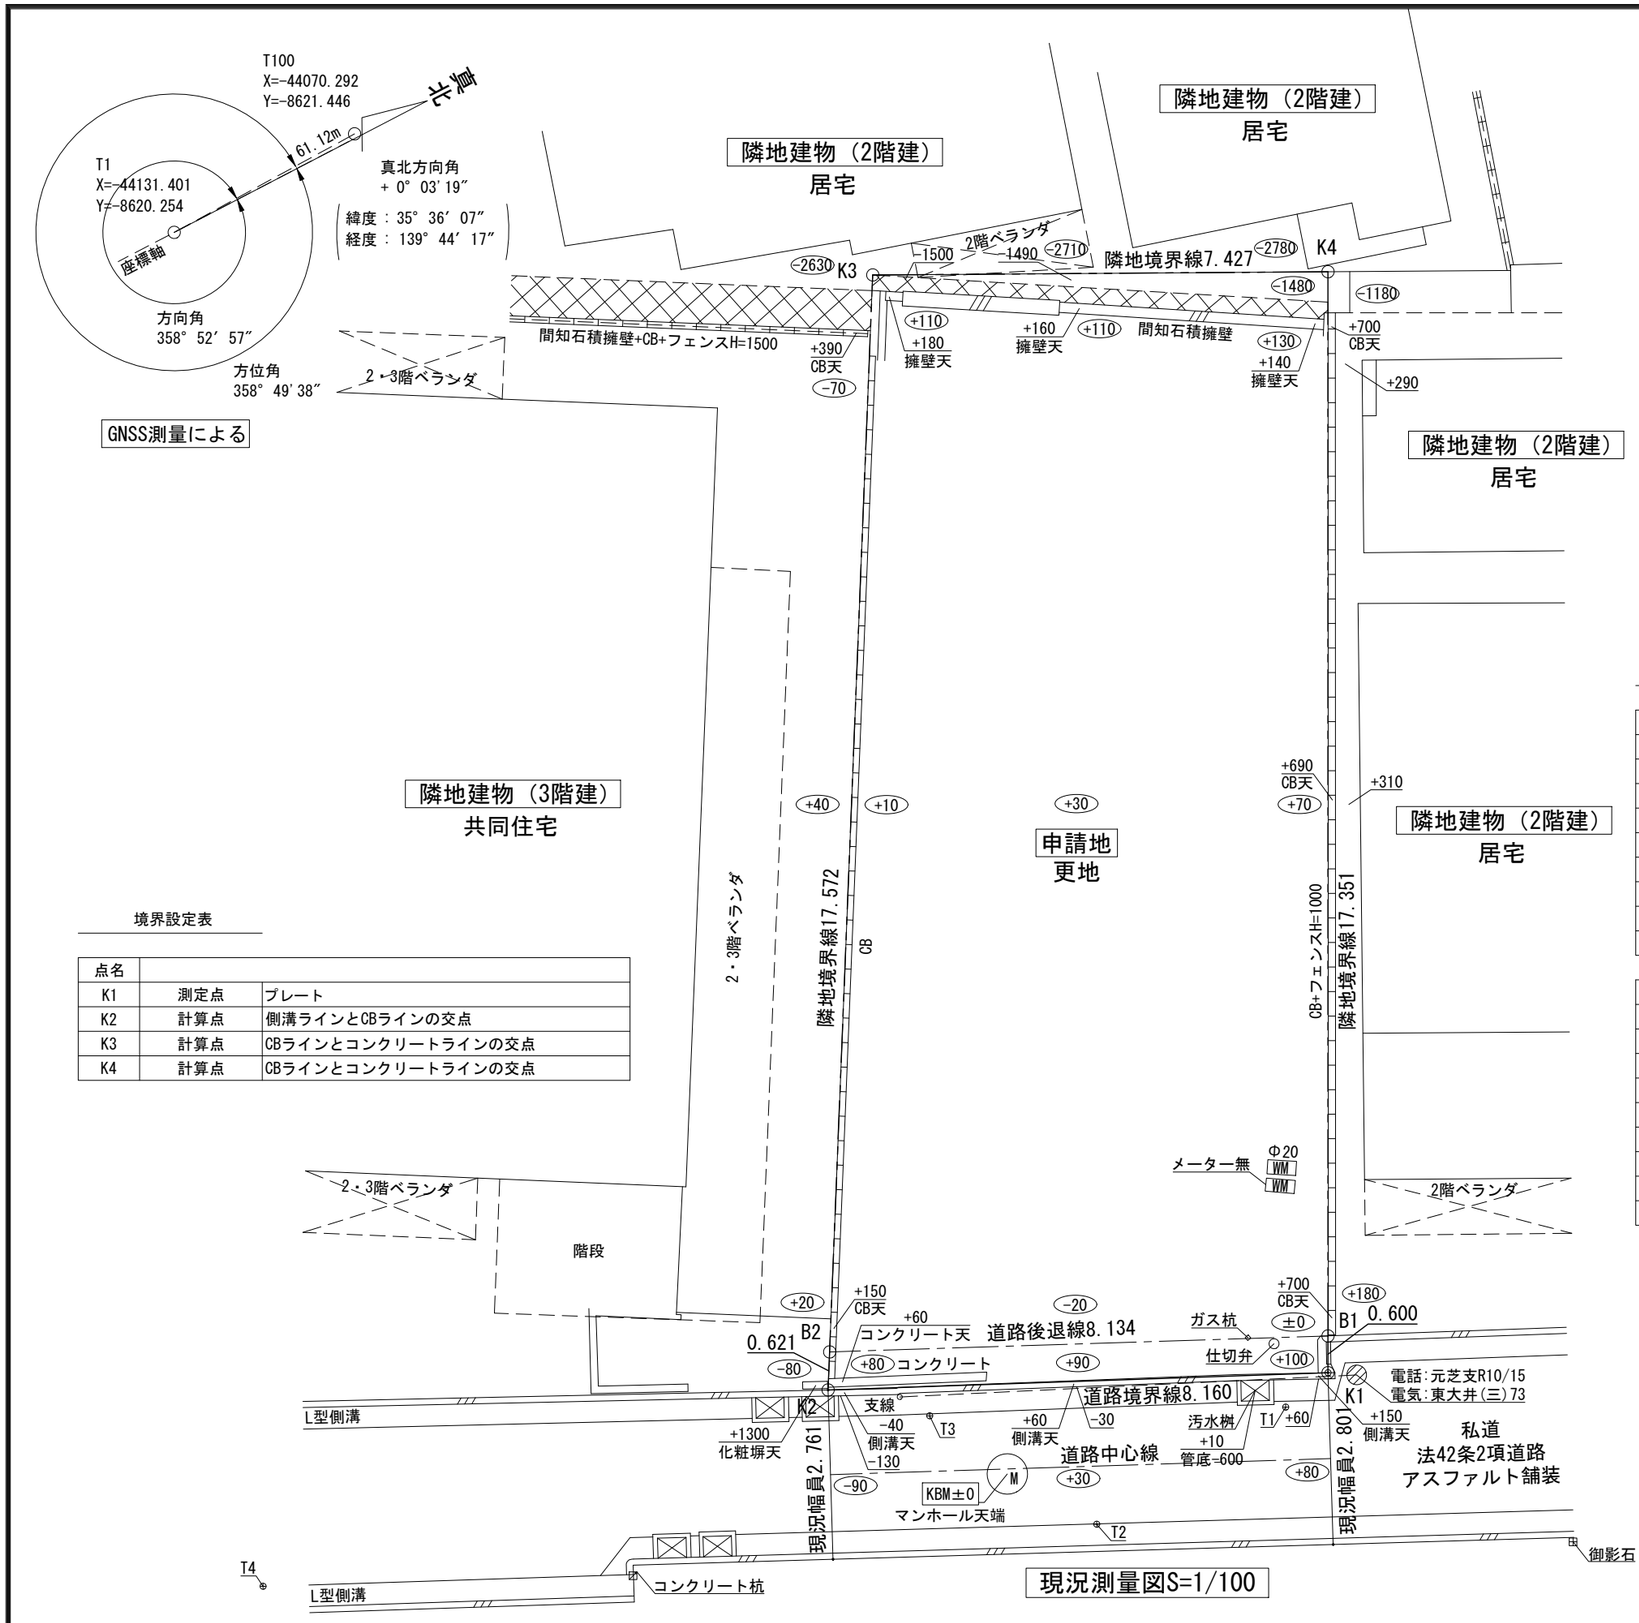


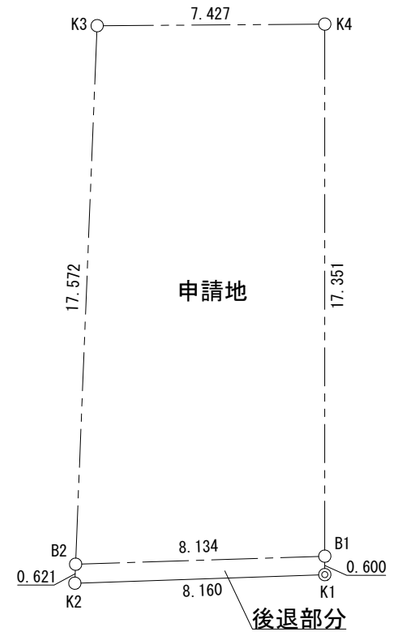

敷地求積図S=1/200

求積表

	申請地			
NO	Xn	Yn	Yn+1-Yn-1	Xn・(Yn+1-Yn-1)
B1	-44130.252	-8620.965	11.865	-523605.439980
B2	-44137.583	-8624.489	-18.772	828550.708076
K3	-44128.850	-8639.737	-11.865	523588.805250
K4	-44122.238	-8636.354	18.772	-828262.651736
			合　計	271.4216100
			合計面積	135.7108050
			地　積	135.71㎡
			坪　数	41.05坪

	後退部分			
NO	Xn	Yn	Yn+1-Yn-1	Xn・(Yn+1-Yn-1)
K1	-44130.529	-8620.433	-2.985	131729.629065
K2	-44137.892	-8623.950	-4.056	179023.289952
B2	-44137.583	-8624.489	2.985	-131750.685255
B1	-44130.252	-8620.965	4.056	-178992.302112
			合　計	9.9316500
			合計面積	4.9658250
			地　積	4.96㎡
			坪　数	1.50坪

合計面積	140.67㎡
合計坪数	42.55坪

境界設定表

点名		
K1	測定点	プレート
K2	計算点	側溝ラインとCBラインの交点
K3	計算点	CBラインとコンクリートラインの交点
K4	計算点	CBラインとコンクリートラインの交点

点名	X 座標	Y 座標
T1	-44131.401	-8620.254
T2	-44135.017	-8619.984
T3	-44136.617	-8622.811
T4	-44147.544	-8625.368

※本図面は現況に基づき測量し作成した図面です。
境界については実際の位置と異なる場合があります。
境界の正規位置については、隣地土地の所有者との相互立会いにより確定させる必要があります。

3D点群データはコチラ

URL Sphere XG

株式会社住ま居る	測量製図担当 株式会社ＪＦＤエンジニアリング	設計者	営業担当	検　図	製　図	作成日	令和7年6月9日
						変更・訂正日	
						変更・訂正日	
						変更・訂正日	

工事名	品川区東大井3丁目785-5 新築工事	図番	
図　名	現 況 図	枚数	