表示年月日：２０２５／０６／０４

イ　748-3　ハ　753-17　ホ　813-11　ト　813-14　リ　813-9　ル　847-22
ロ　749-23　ニ　753-23　ヘ　813-13　チ　813-5　ヌ　846-12　つづく

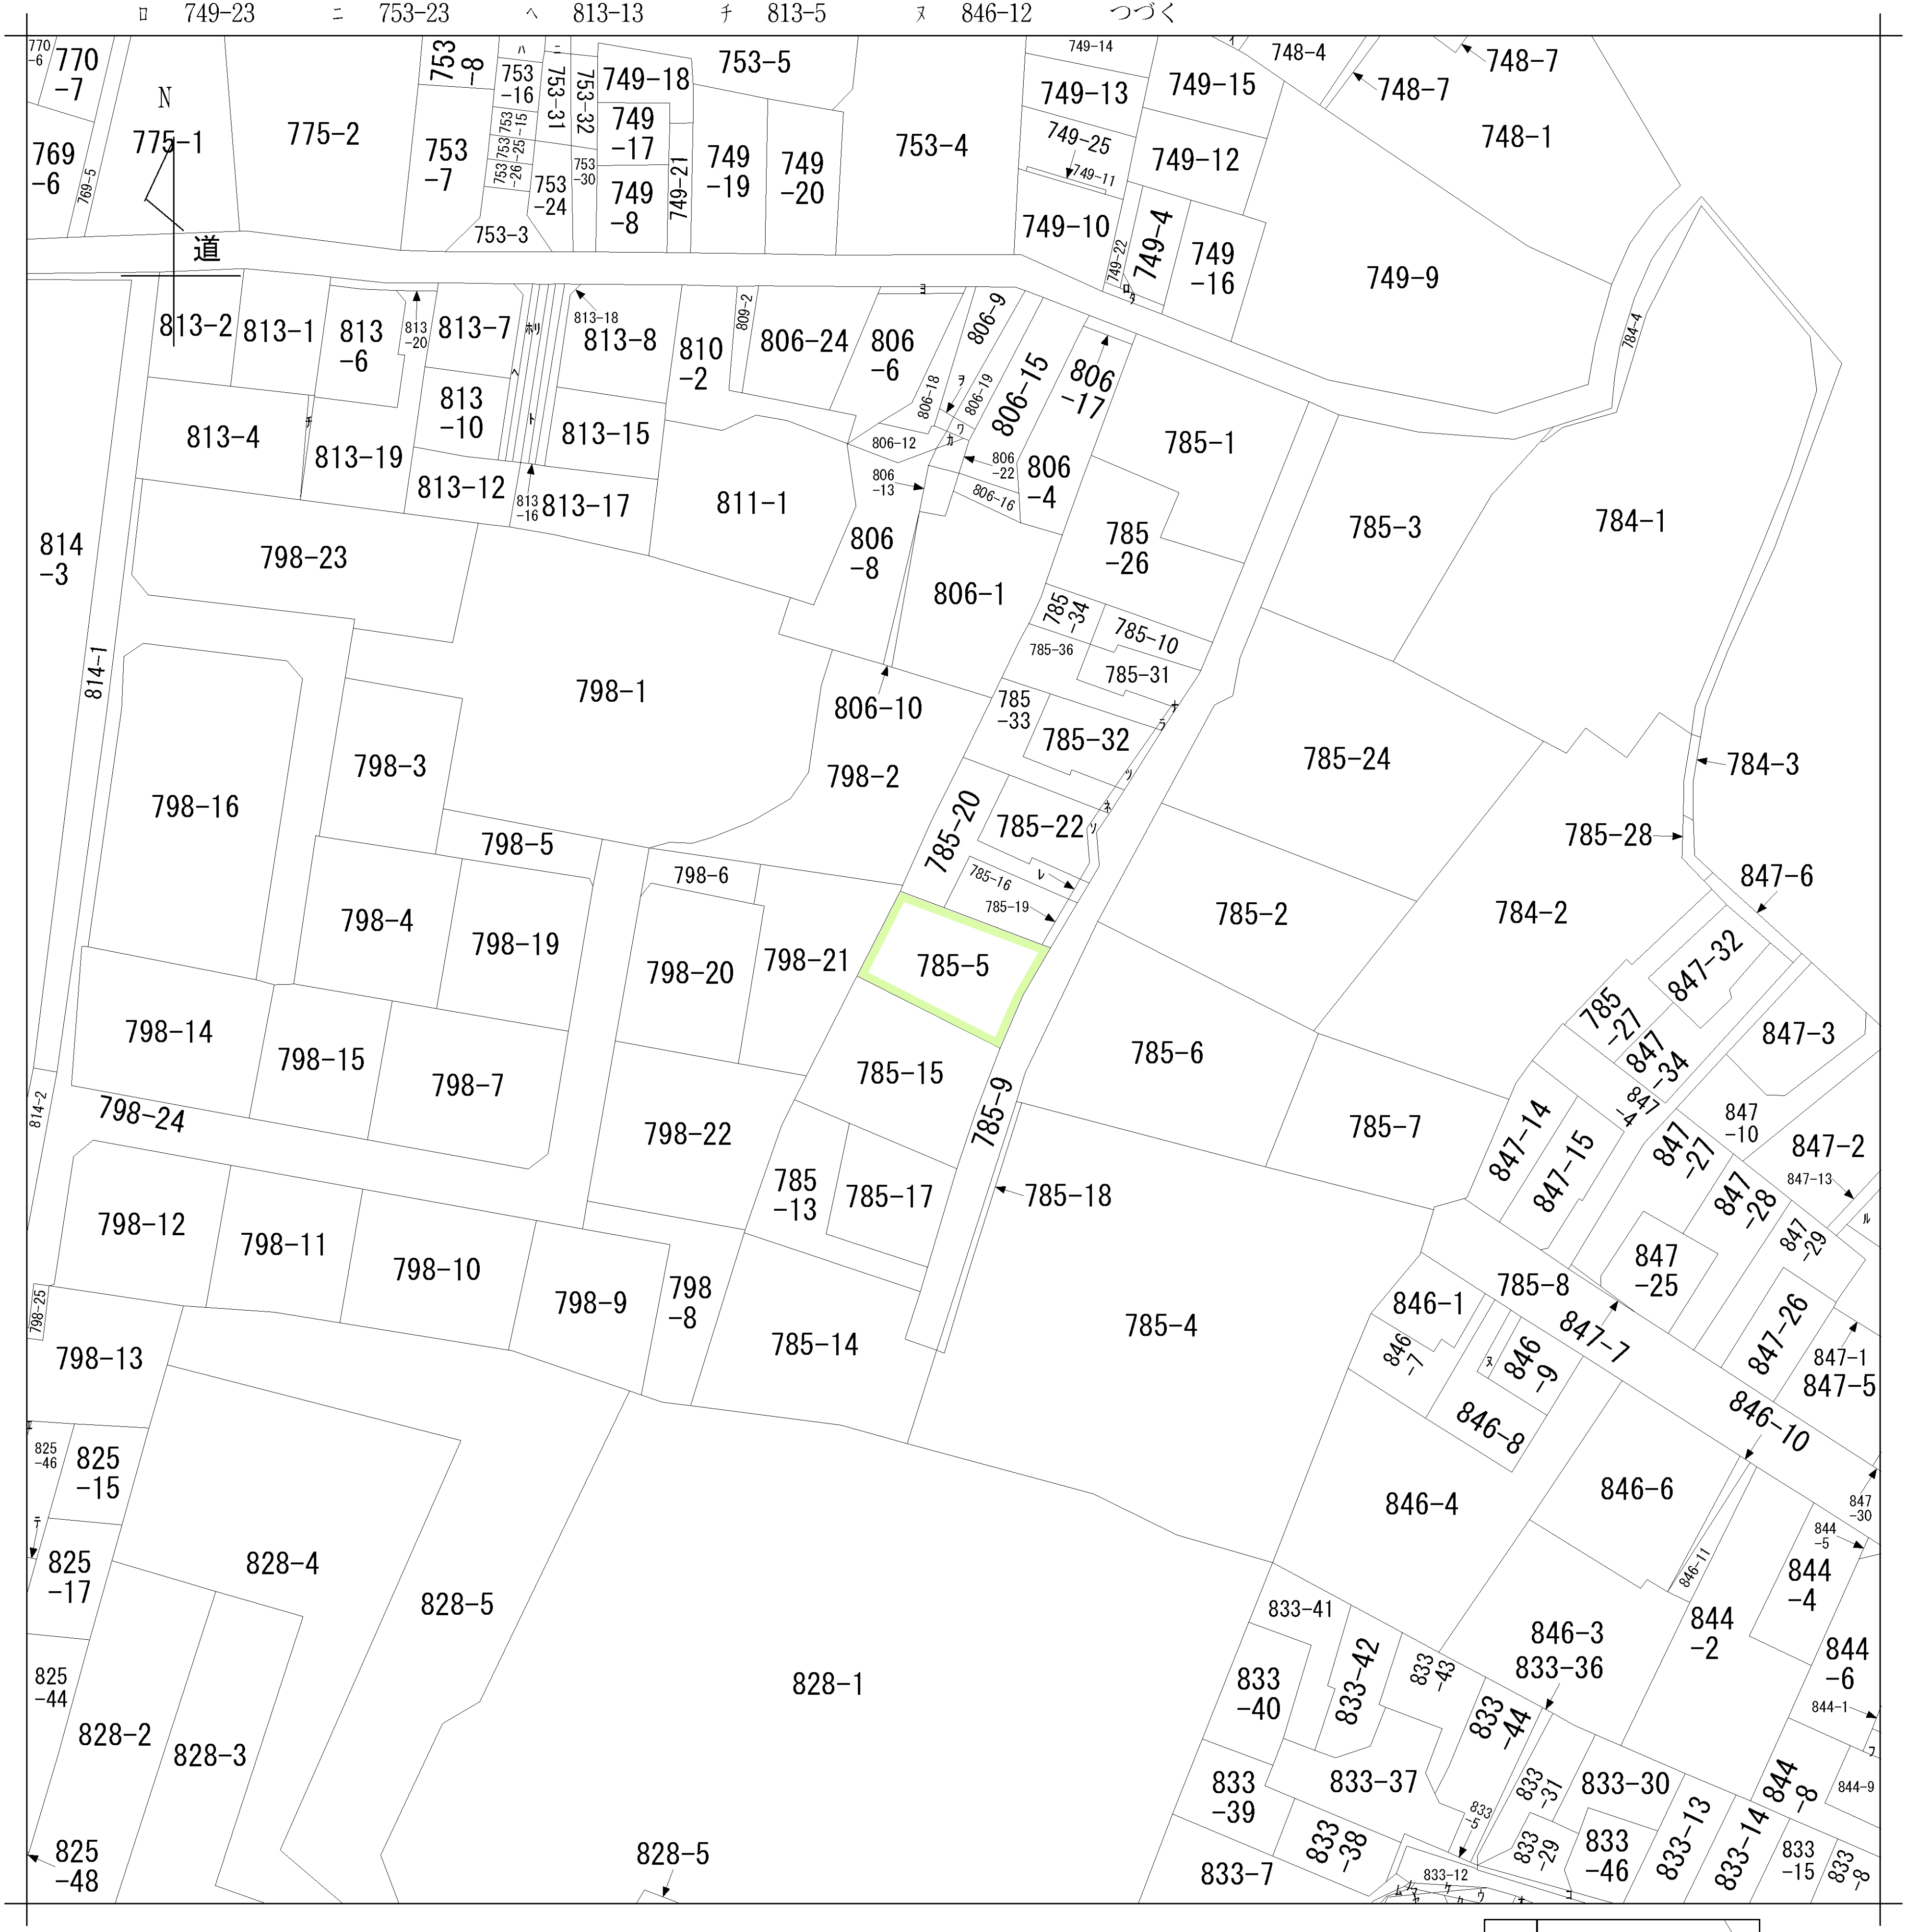

地番区域見出し	東大井３丁目

請求部分	所在	品川区東大井三丁目					地番	785番5	
出力縮尺	1/600	精度区分		座標系番号又は記号		分類	地図に準ずる図面	種類	旧土地台帳附属地図
作成年月日		備付年月日（原図）		補記事項					

ｦ	806-14
ﾜ	806-23
ｶ	806-20
ﾖ	806-25
ﾀ	749-24
ﾚ	785-21
ｿ	785-23
ﾂ	785-29
ﾈ	785-30
ﾅ	785-12
ﾗ	785-35
ﾑ	833-1
ｳ	833-16
ﾉ	833-17
ｵ	833-19
ｸ	833-2
ﾔ	833-26
ﾏ	833-27
ｹ	833-28
ﾌ	844-7
ｺ	833-10
ｴ	825-45
ﾃ	825-47

２０２５／０６／０４　１８：１３　現在の情報です。

表題部　（土地の表示）		調製	平成７年１１月２２日	不動産番号	０１０７０００１５２４１６
地図番号	余白	筆界特定	余白		
所在	品川区東大井三丁目				余白

①地番	②地目	③地積　町　反　畝　歩(坪)　㎡	原因及びその日付〔登記の日付〕
７８５番5	宅地	(旧)　４０５：２０	余白
余白	余白	(旧)　３１５：２０ ：	③本番５、１０、１１、１２に分筆 〔昭和３６年５月２４日〕
余白	余白	(旧)　１７２：６７ ：	③７８５番５、１３、１４に分筆 〔昭和３９年９月５日〕
余白	余白	３６６：５７ ：	③７８５番５、１５に分筆 〔昭和３９年１０月５日〕
余白	余白	１３５：１３ ：	③７８５番５、７８５番１６に分筆 〔昭和４２年５月１５日〕
余白	余白	余白　： ： ：	昭和６３年法務省令第３７号附則第２条第２項の規定により移記 平成７年１１月２２日

権利部（甲区）　（所有権に関する事項）			
順位番号	登記の目的	受付年月日・受付番号	権利者その他の事項
１	所有権移転	昭和５４年３月２日 第５２６７号	原因　昭和５２年７月２８日相続 共有者 品川区東大井三丁目８番３号 持分２分の１ 小松原美枝子 品川区東大井三丁目９番２３号 ２分の１ 三尾章子 順位２番の登記を移記
付記１号	１番登記名義人住所変更	令和５年５月２５日 第１４４５０号	原因　平成５年８月２２日住所移転 共有者三尾章子の住所　東京都三鷹市井の頭一丁目６番２７号
	余白	余白	昭和６３年法務省令第３７号附則第２条第２項の規定により移記 平成７年１１月２２日
２	小松原美枝子持分全部移転	令和５年５月２５日 第１４４５１号	原因　令和４年１２月８日相続 所有者　東京都三鷹市井の頭一丁目６番２７号 持分２分の１ 三尾章子

＊　「登記の目的」欄に「相続人申告」と記載されている登記は、所有権の登記名義人（所有者）の相続人からの申出に基づき、登記官が職権で、申出があった相続人の住所・氏名等を付記したものであり、権利関係を公示するものではない。

＊　下線のあるものは抹消事項であることを示す。

２０２５／０６／０４　１８：１３　現在の情報です。

表題部　（主である建物の表示）	調製	平成７年１１月２２日	不動産番号	０１０７０００１６００２７

所在図番号	余 白		
所　在	品川区東大井三丁目　７８５番地５		余 白
家屋番号	７８５番５		余 白
①　種　類	②　構　造	③　床　面　積　㎡	原因及びその日付〔登記の日付〕
共同住宅	木造瓦葺２階建	１階　６６：１０ ２階　６６：１０	昭和４６年８月３１日新築
余 白	余 白	余 白　： ： ：	昭和６３年法務省令第３７号附則第２条第２項の規定により移記 平成７年１１月２２日

権　利　部　（　甲　区　）　（所　有　権　に　関　す　る　事　項）			
順位番号	登　記　の　目　的	受付年月日・受付番号	権　利　者　そ　の　他　の　事　項
１	所有権保存	昭和４６年９月３０日 第２４１３８号	共有者 品川区東大井三丁目８番３号 持分２分の１ 小　松　原　豊 品川区東大井三丁目８番３号 ２分の１ 小　松　原　美　枝　子 順位１番の登記を移記
２	小松原豊持分全部移転	昭和５４年３月２日 第５２７４号	原因　昭和５２年７月２８日相続 共有者 品川区東大井三丁目８番３号 持分４分の１ 小　松　原　美　枝　子 品川区東大井三丁目９番２３号 ４分の１ 三　尾　章　子 順位２番の登記を移記
付記１号	２番登記名義人住所変更	令和５年５月２５日 第１４４５０号	原因　平成５年８月２２日住所移転 共有者三尾章子の住所　東京都三鷹市井の頭一丁目６番２７号
	余 白	余 白	昭和６３年法務省令第３７号附則第２条第２項の規定により移記 平成７年１１月２２日
３	小松原美枝子持分全部移転	令和５年５月２５日 第１４４５２号	原因　令和４年１２月８日相続 所有者　東京都三鷹市井の頭一丁目６番２７号 持分４分の３ 三　尾　章　子

＊　「登記の目的」欄に「相続人申告」と記載されている登記は、所有権の登記名義人（所有者）の相続人からの申出に基づき、登記官が職権で、申出があった相続人の住所・氏名等を付記したものであり、権利関係を公示するものではない。

＊　下線のあるものは抹消事項であることを示す。

土地所在図
地積測量図

地番	㊊785 785[illegible]～-5 16
土地の所在	品川区東大井参丁目

作製年月日	昭和四拾弐年五月拾日
作製者	東京都品川区北品川弐丁目参弐番壱七号 土地家屋調査士 坂井 正 電話白金(四七二)四〇一八番
申請	小松原 豊

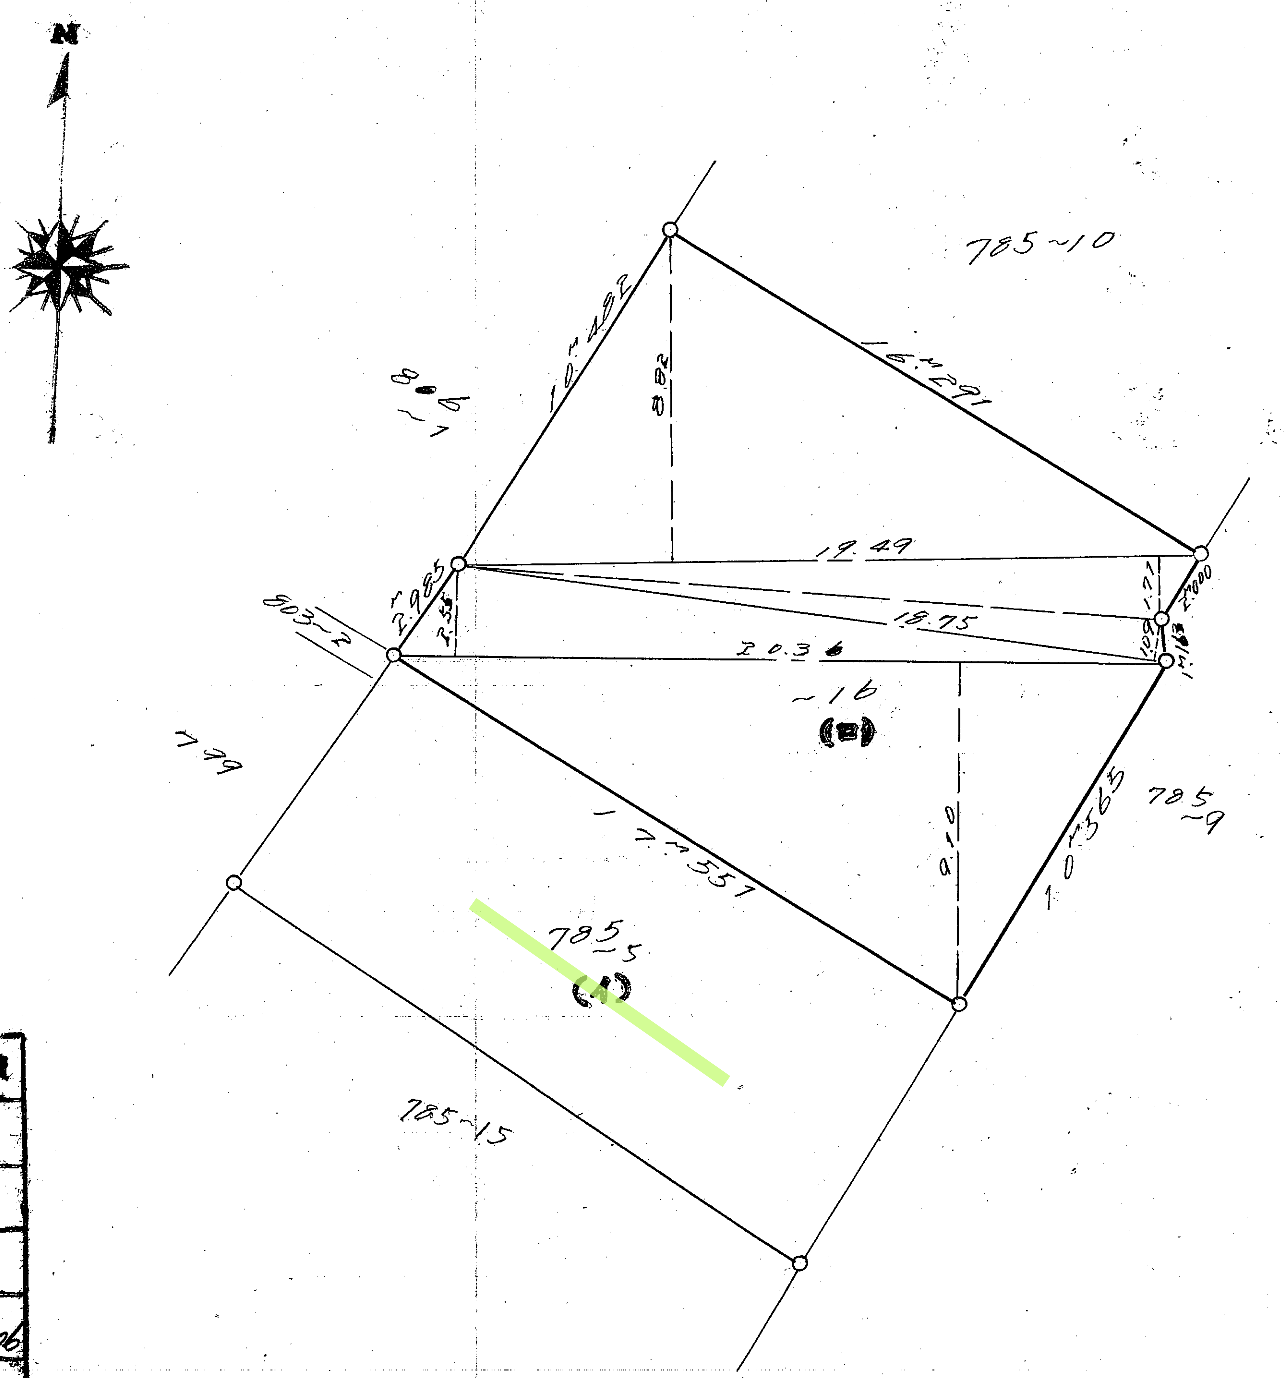

面積計算表

地番	符合	底辺	垂線	倍面積	面積
785-16	(ロ)	19.49	8.82 1.71	205.2297	
		18.75	1.09	20.4375	
		20.36	9.10 2.55	237.1940	
				462.8612	m² 231.4306
785-5	(イ)				m² 135.1394

縮尺	1/	1/200

230734

(全国土地家屋調査士会連合会用紙)

昭和四拾弐年五月拾五日

S42.5.15.

建物図面
各階平面図

家屋番号	785～5
建物の所在	東京都　品川区　東大井3丁目　785番地　5

1階平面図

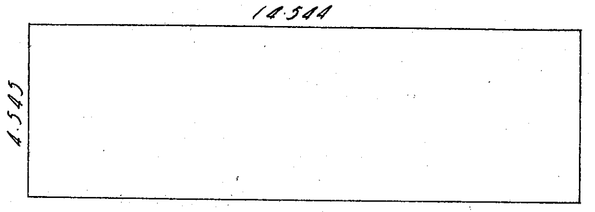

2階平面図

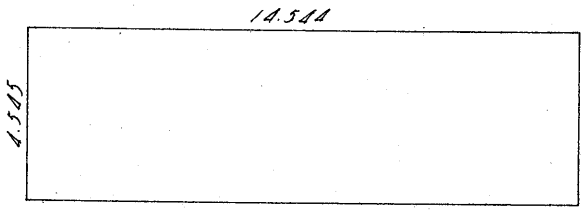

1・2階求積表

14.544×4.545＝66.1024㎡

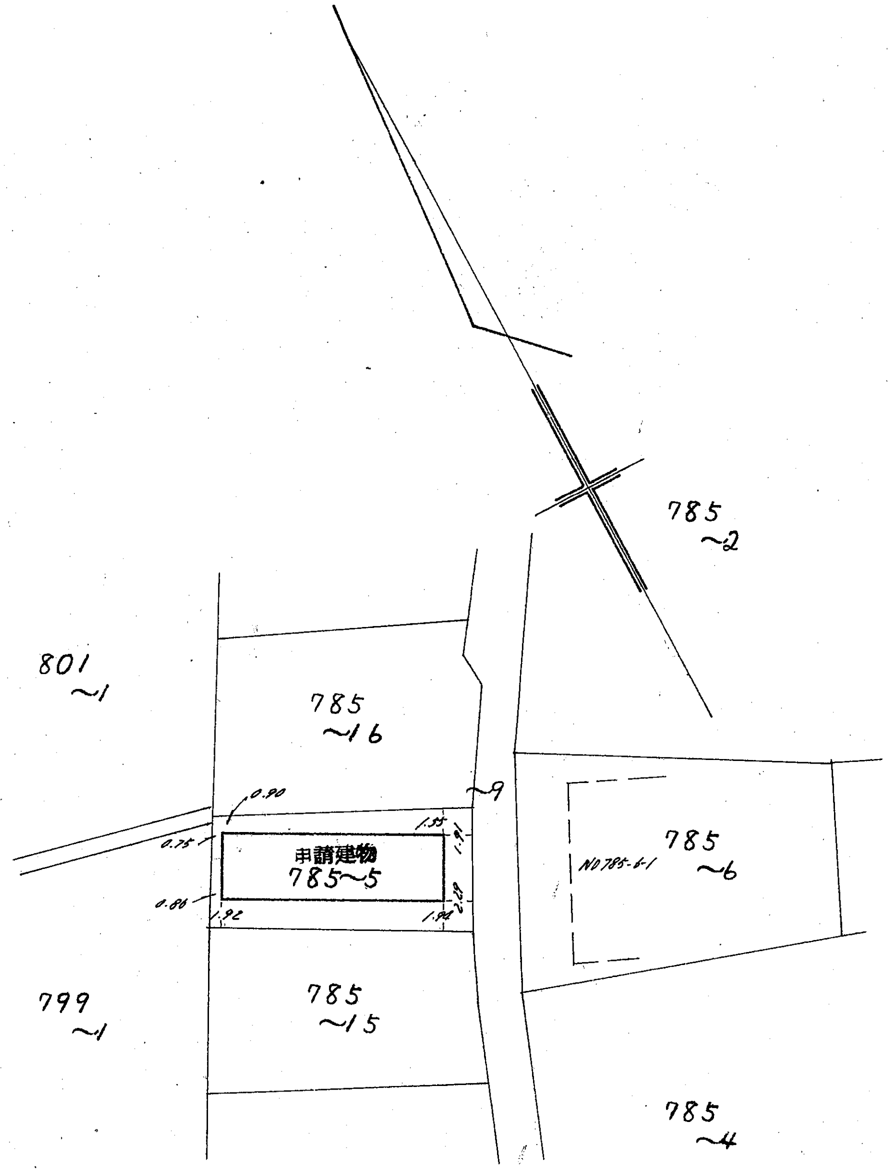

119236

縮尺	1/200　1/500

作製年月日	昭和46年9月28日
作製者	東京都葛飾区東堀切弐丁目拾五番弐 土地家屋調査士　内田孝
申請人	持分弐分壱　小松原豊 持分弐分壱　小松原美枝子

昭和四拾六年九月弐拾九日

S46.9.29